

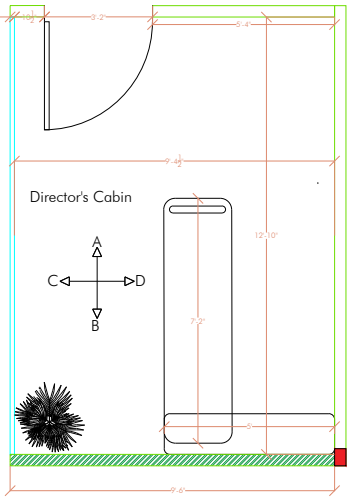


Floor Plan

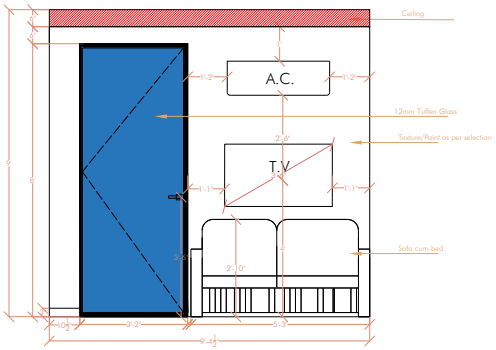


Elevation-A

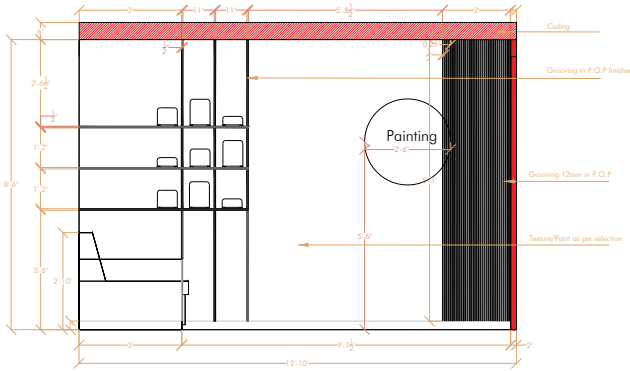

Elevation-D



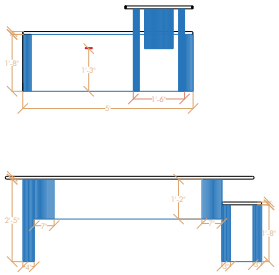

Furniture Drawings

N

DATE	REVISION	BY

Key Plan :

PROJECT : 001

CLIENT : Mr. RISHAV

DRAWING TITLE : Director's Cabin Elv. 1

SCALE : 1:100

VERSION : 01

DATE : 02-12-2025

DRAWN BY : JATIN KUMAR

Checked BY : Ar. AYUSHI JALAN

studio intange

Email : intange.business@gmail.com
Ar. Ayushi Jalan
+91-9833877050