
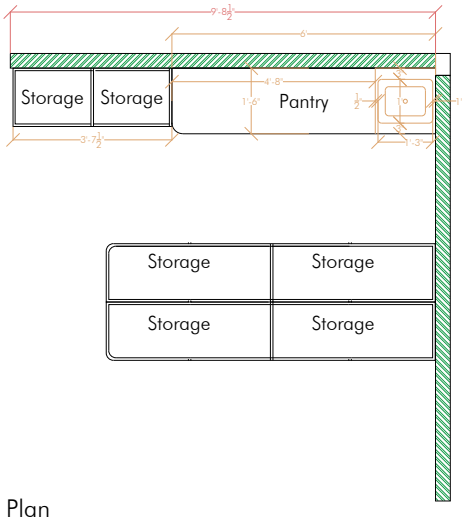


Pantry Plan

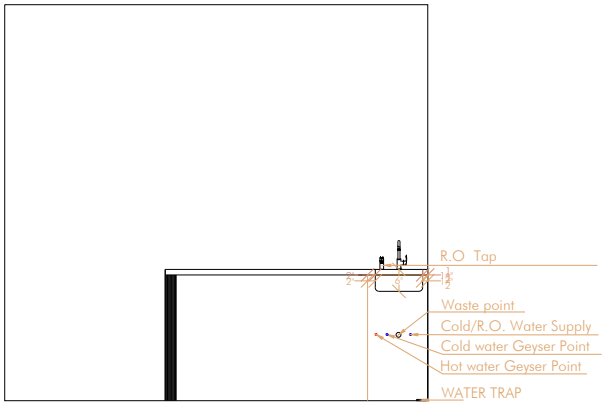

Plumbing Plan

Sr. No.	Symbols	Descriptions
1.		Hot Water Line
2.		Cold Water Line

Note: All CP Fittings From Kohler X Series of body color Matt Gold As per Selection
All Sanitary fittings from Kohler In white body As per Selection

DATE	REVISION	BY

Key Plan :

PROJECT : 001

CLIENT :
Mr. RISHAV

DRAWING TITLE :
Plumbing

SCALE : 1:100

VERSION : 01

DATE : 25-11-2025

DRAWN BY :
JATIN KUMAR

Checked BY :
Ar. AYUSHI JALAN

studio intange

Email : intange.business@gmail.com
Ar. Ayushi Jalan
+91-9833877050